
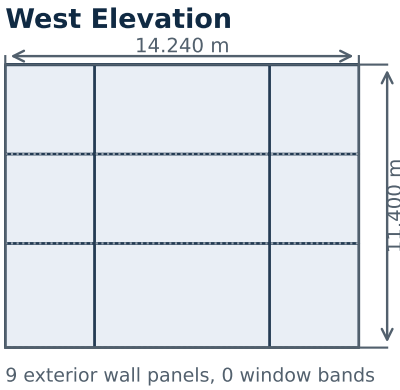
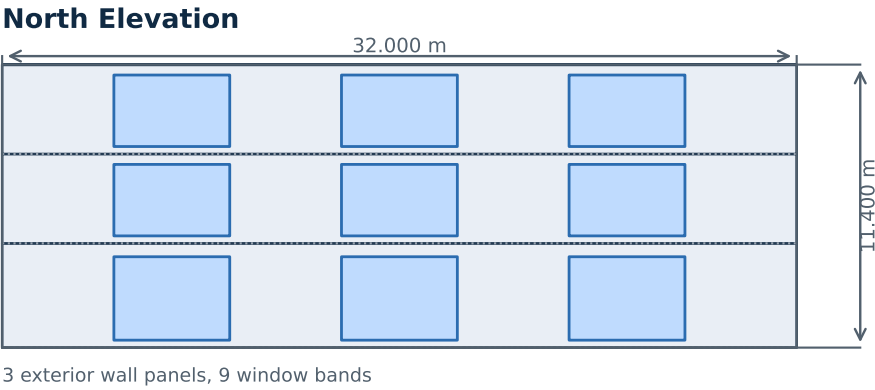
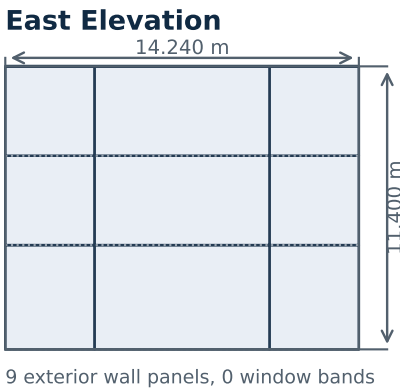
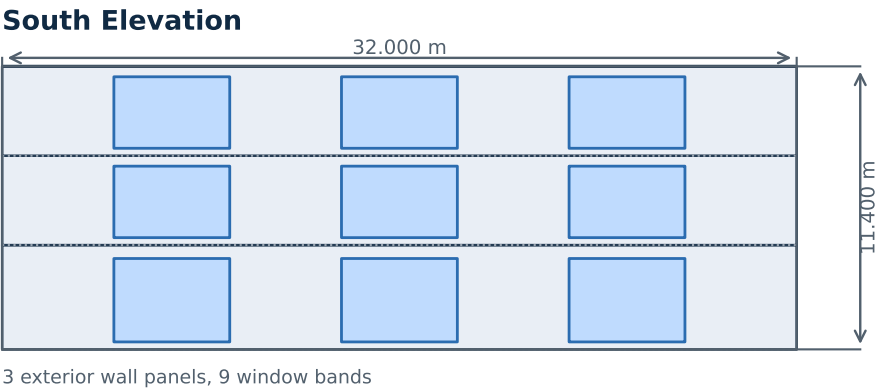
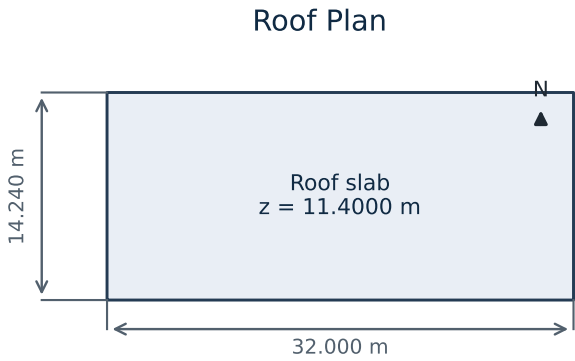
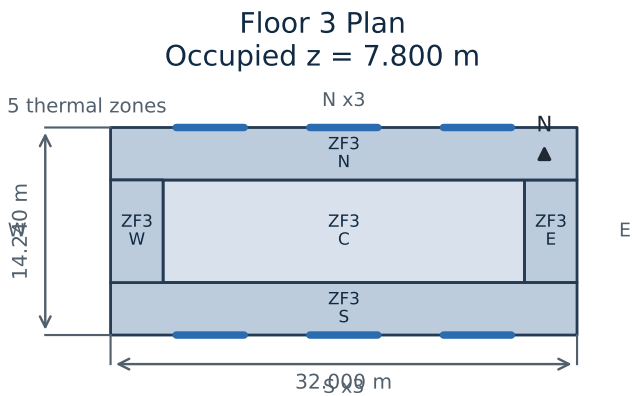
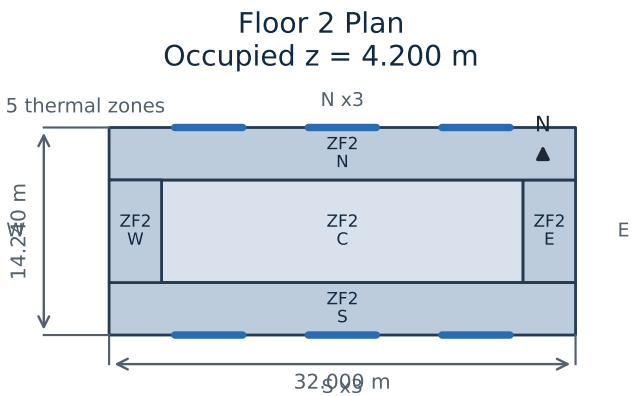


IDF-Derived Medium Office Building Structure


Plan, roof, facade, and section views reconstructed from EnergyPlus model geometry

Model Summary

Occupied stories: 3
Footprint: 32.000 m x 14.240 m
Roof elevation: 11.4000 m
Occupied levels: 0.000, 4.200, 7.800 m
Plenum levels: m
Facade window bands: 18
Window orientations: South 9, North 9
Envelope surfaces: Wall 60, Floor 15, Ceiling 10, Roof 5

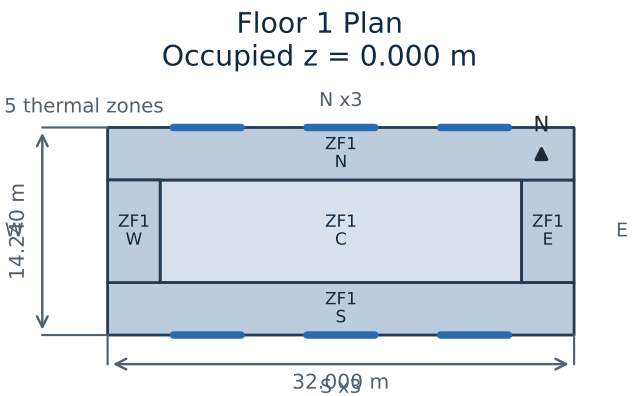

Sectional Story Stack

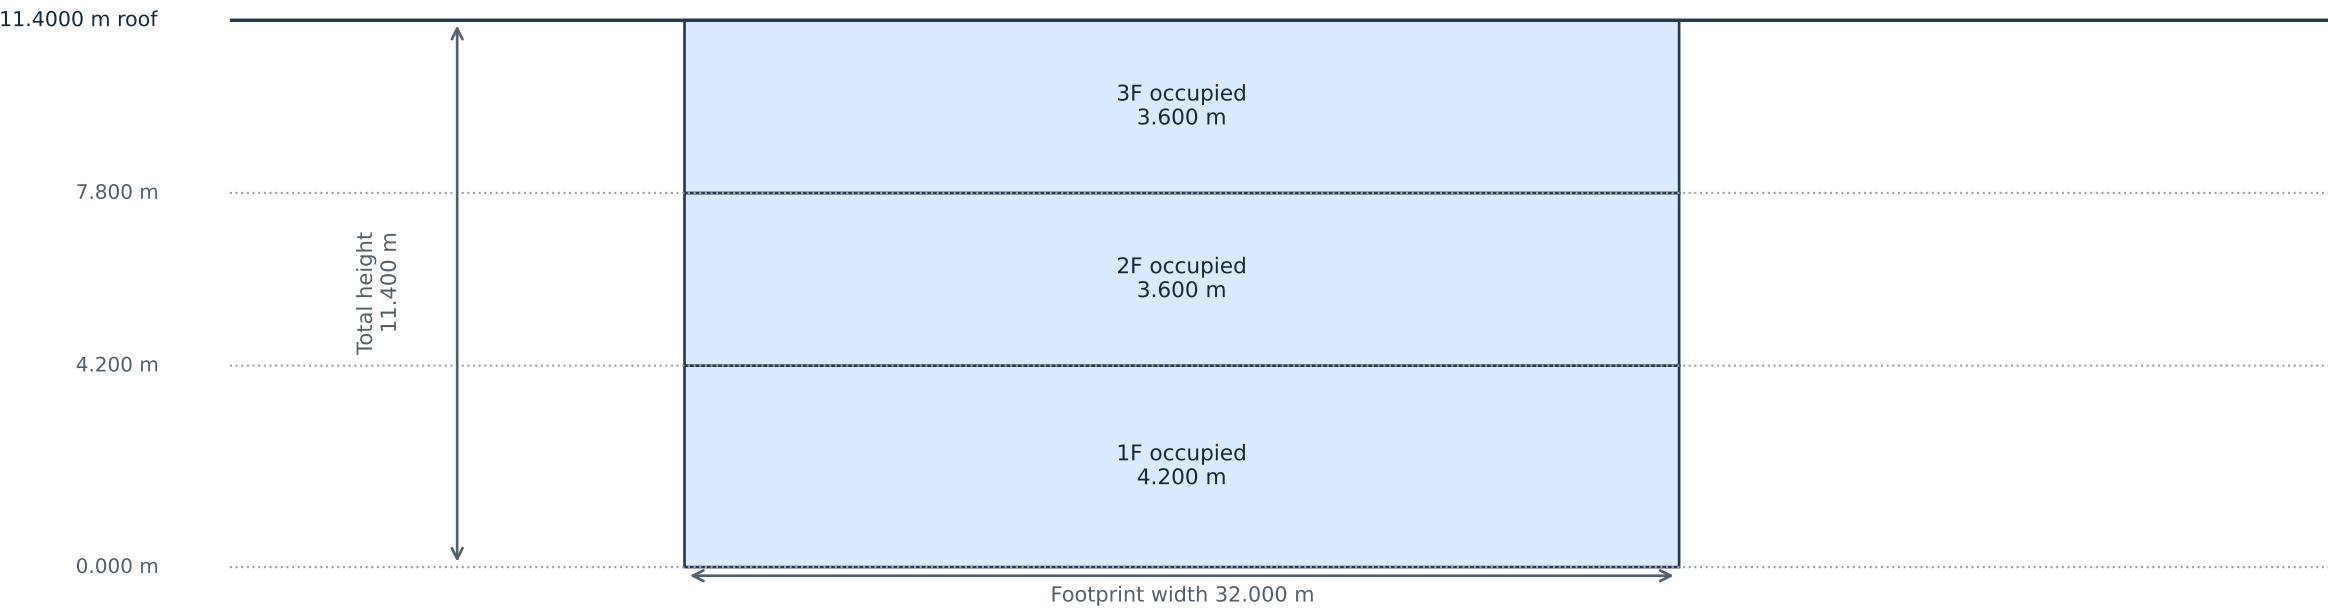

- Core zone
- Perimeter zone
- Plenum footprint
- Facade window band
- Occupied section