


FCU + DOAS Service Overlay

System topology overlaid on plan, roof, facade, and section views

FCU + DOAS Service Overlay

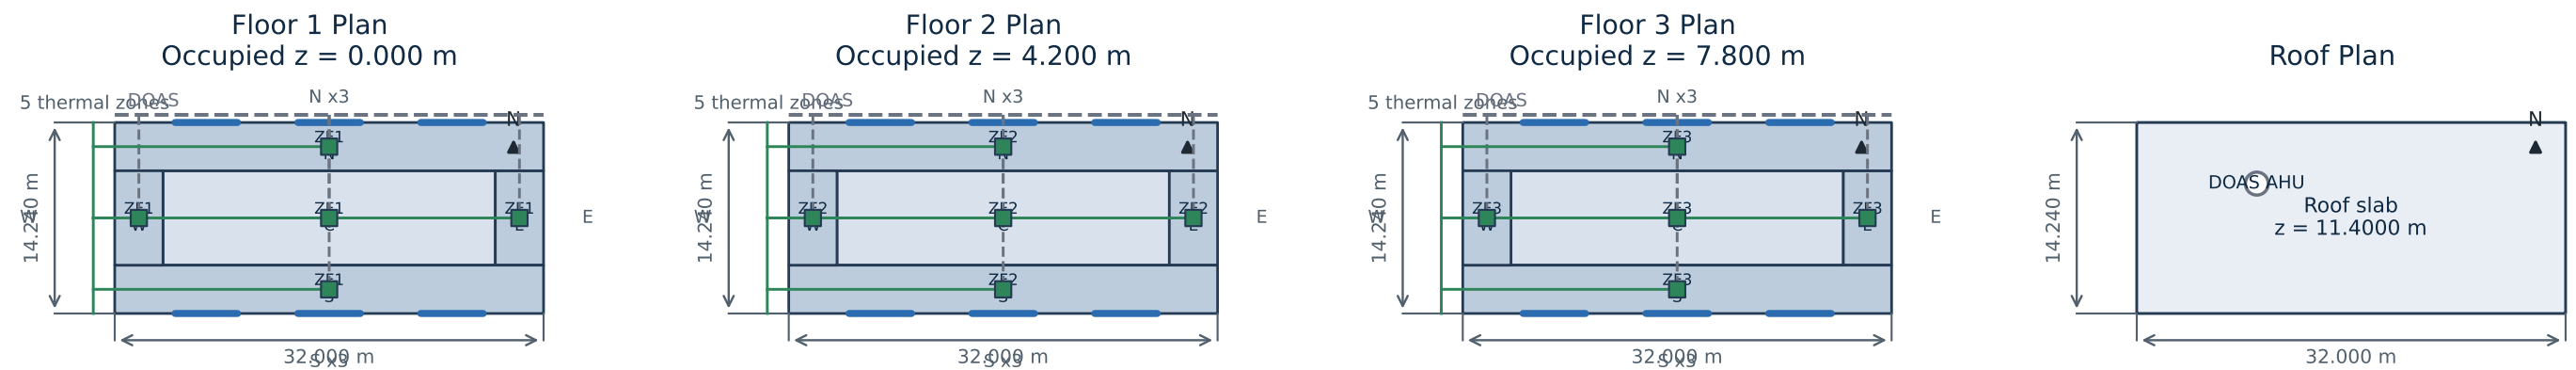


Occupied stories served: 3
Per-floor terminals: 5
Model total terminals: 15
Roof equipment: DOAS AHU
Outdoor air distribution: one main spine plus zone branches
Vertical service: CHW/HW riser
Section emphasis: separated DOAS duct shaft and CHW/HW pipe shaft
Building footprint: 32.000 m x 14.240 m
Roof elevation: 11.4000 m

South Elevation




3 exterior wall panels, 9 window bands

East Elevation

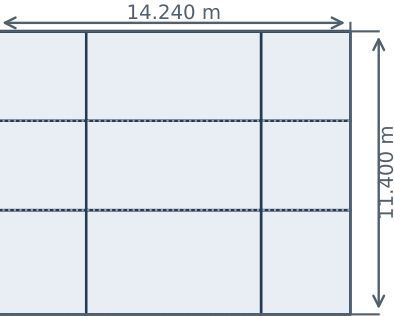


9 exterior wall panels, 0 window bands

North Elevation

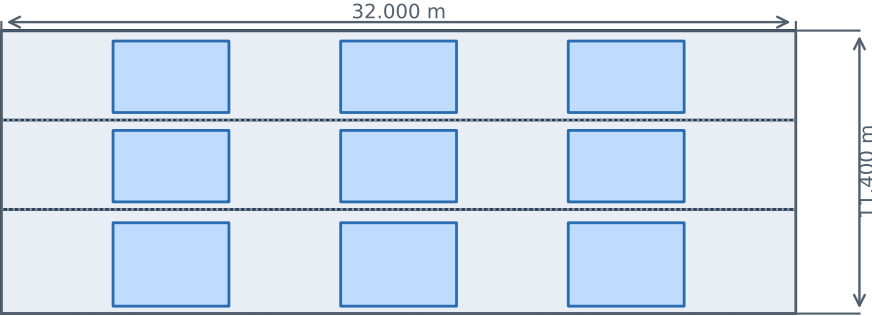

3 exterior wall panels, 9 window bands


West Elevation

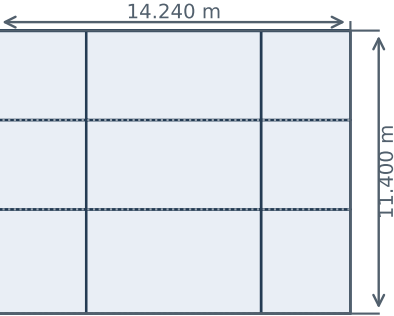

9 exterior wall panels, 0 window bands

One fan-coil terminal per conditioned zone
Dedicated outdoor air spine and branch drops
Compact CHW/HW riser indicates plant-side service to floor terminals

Sectional Story Stack

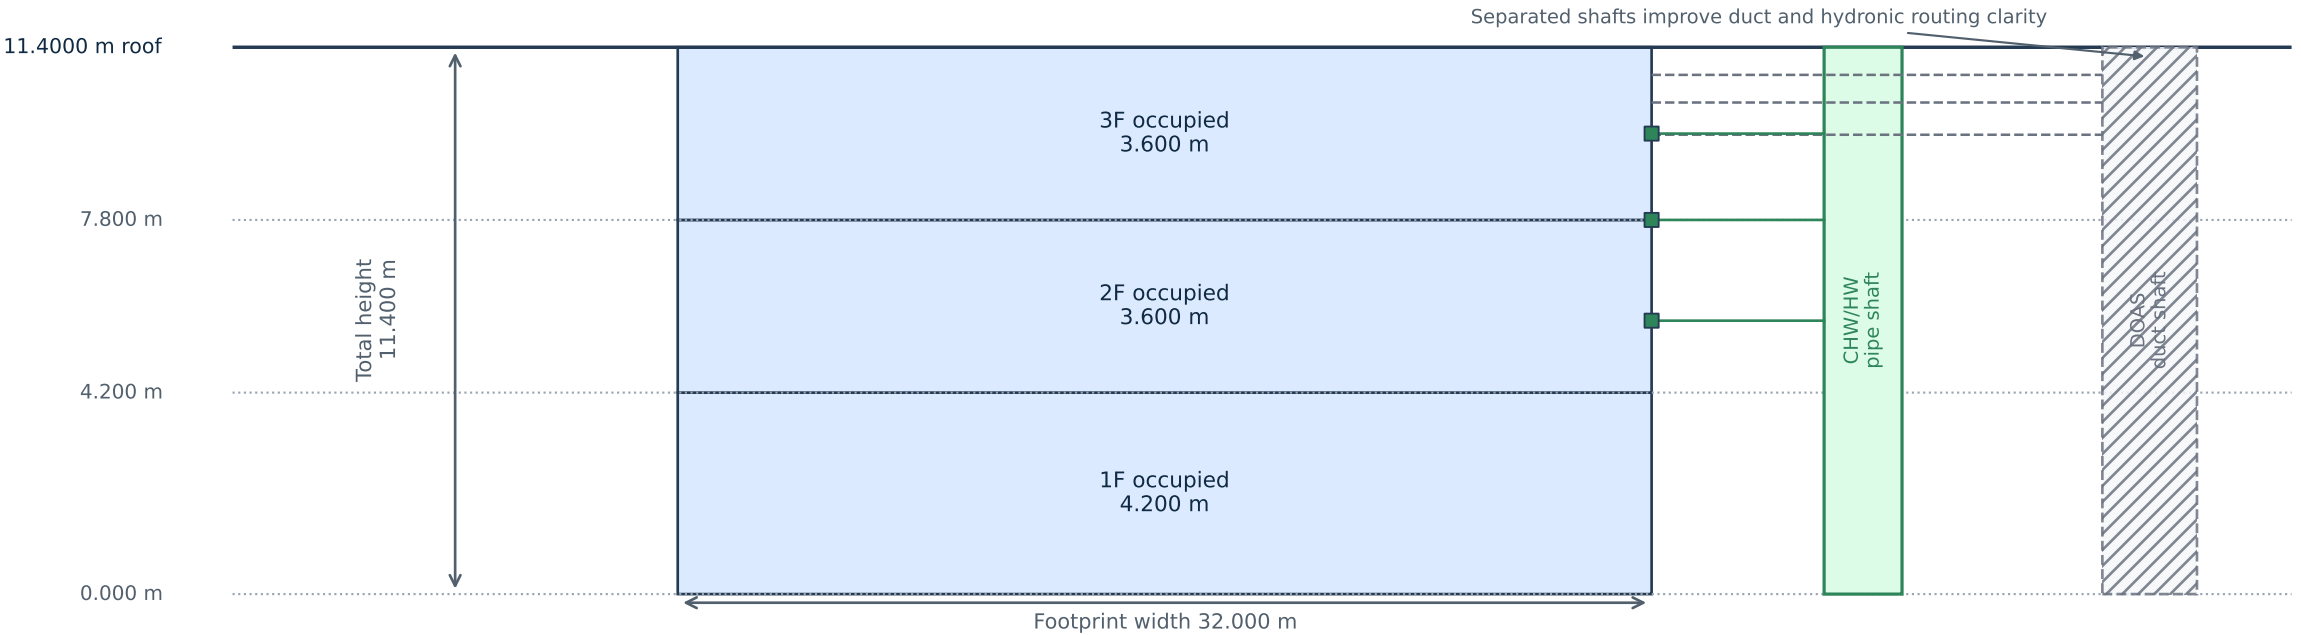

- Conditioned zone
- DOAS duct / shaft
- CHW/HW riser
- One fan-coil terminal per conditioned zone