


VRF + DOAS Service Overlay


System topology overlaid on plan, roof, facade, and section views

VRF + DOAS Service Overlay

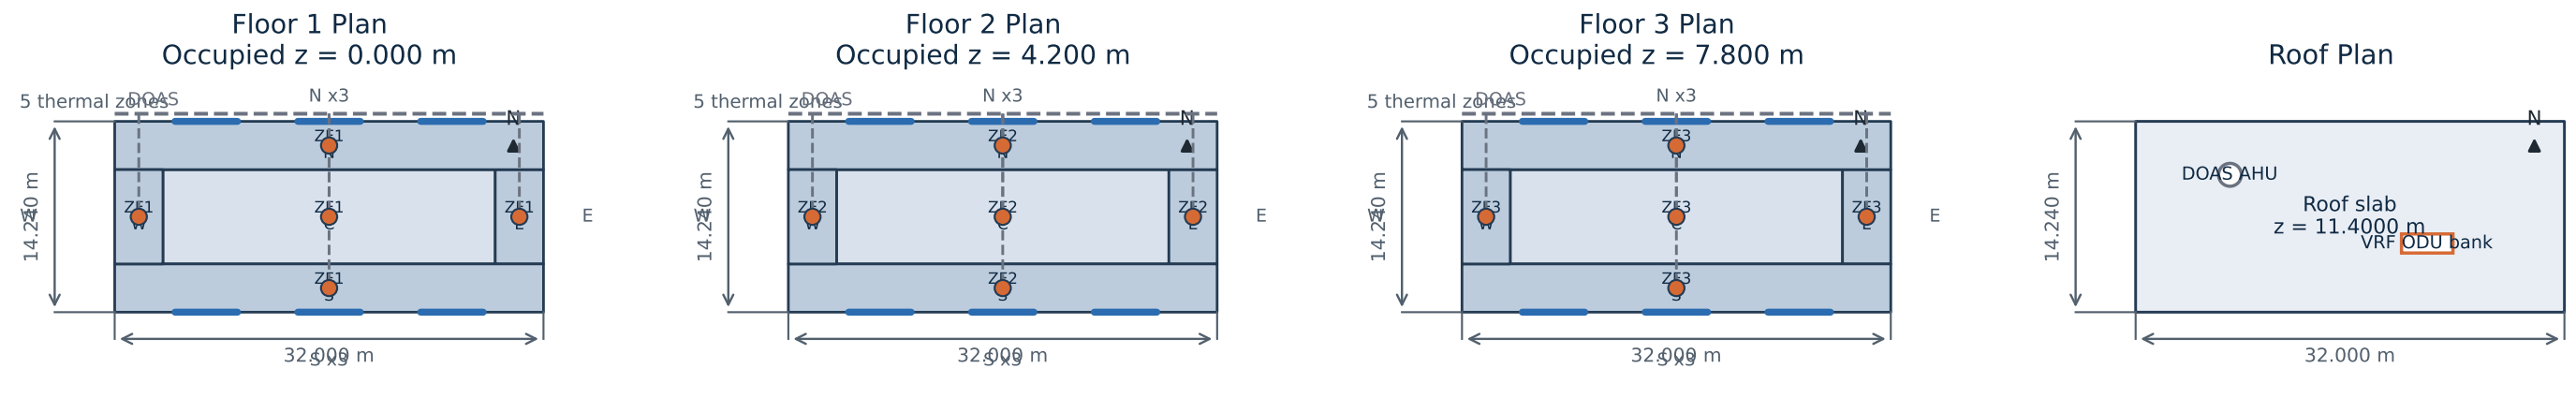


Occupied stories served: 3
Per-floor terminals: 5
Model total terminals: 15
Roof equipment: DOAS AHU, VRF ODU bank
Outdoor air distribution: one main spine plus zone branches
Vertical service: Refrigerant riser
Facade emphasis: concentrated rooftop ODU bank on south elevation
Building footprint: 32.000 m x 14.240 m
Roof elevation: 11.4000 m


South Elevation

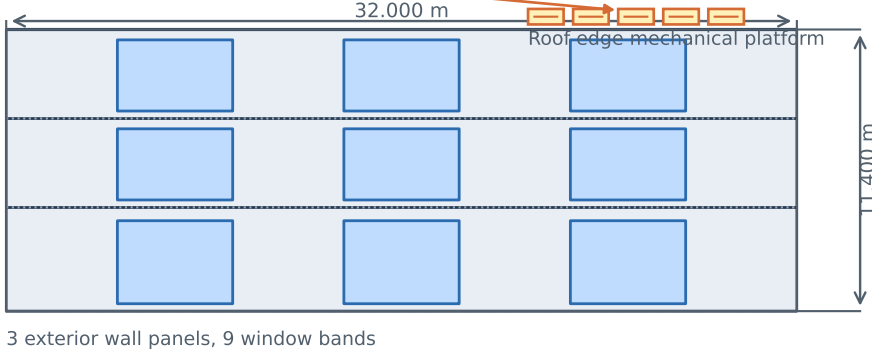


East Elevation

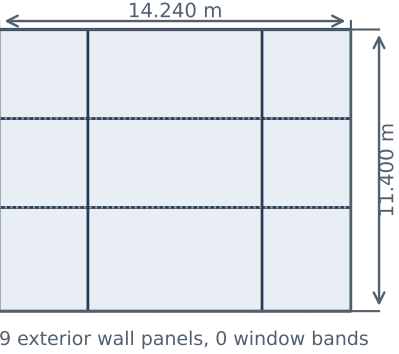

North Elevation

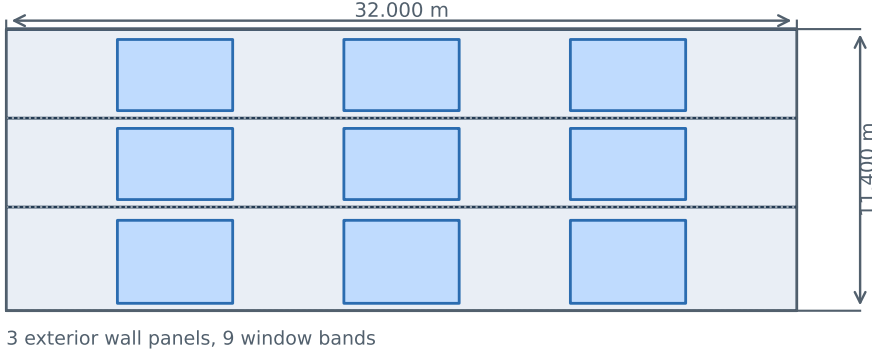


West Elevation

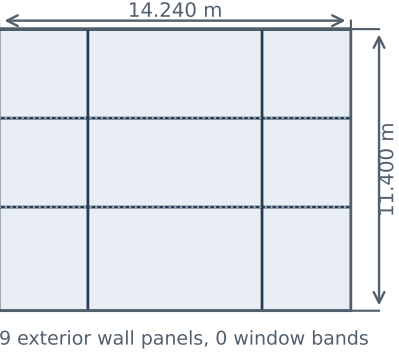

One VRF terminal per conditioned zone
Dedicated outdoor air spine and branch drops
Shared VRF outdoor unit serves all terminals on the model branch

Sectional Story Stack

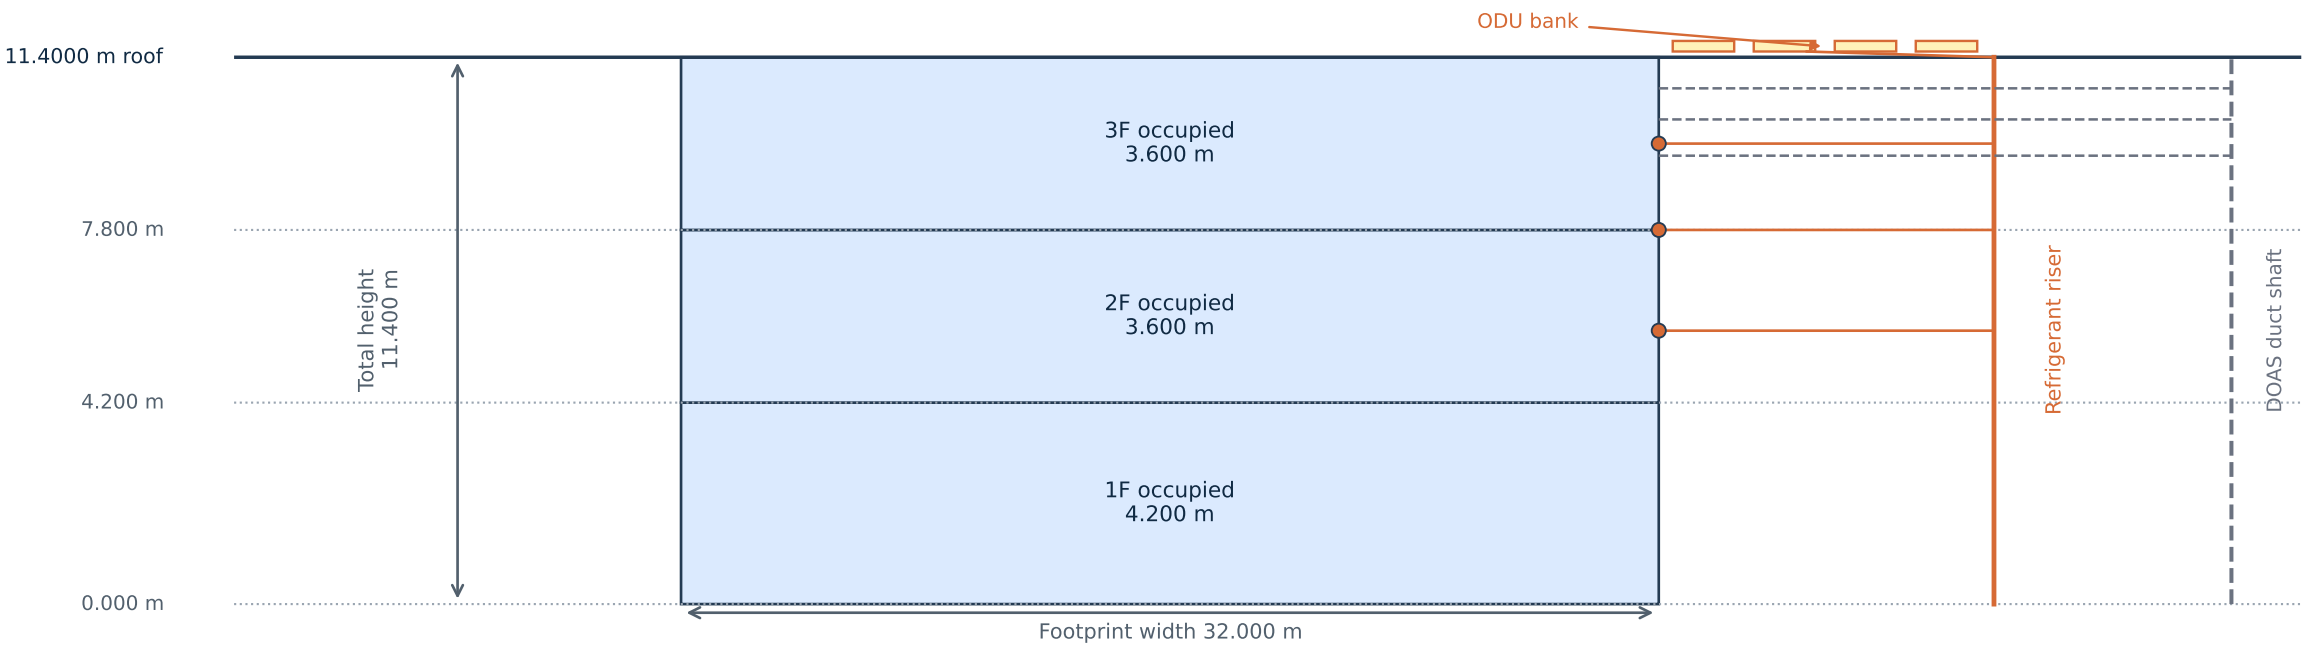

- Conditioned zone
- DOAS duct / shaft
- Refrigerant riser
- One VRF terminal per conditioned zone