
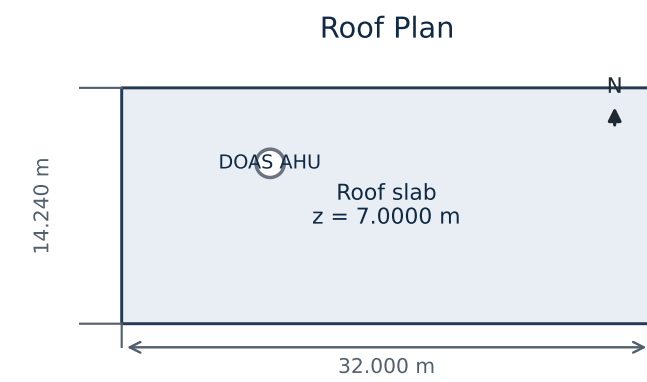
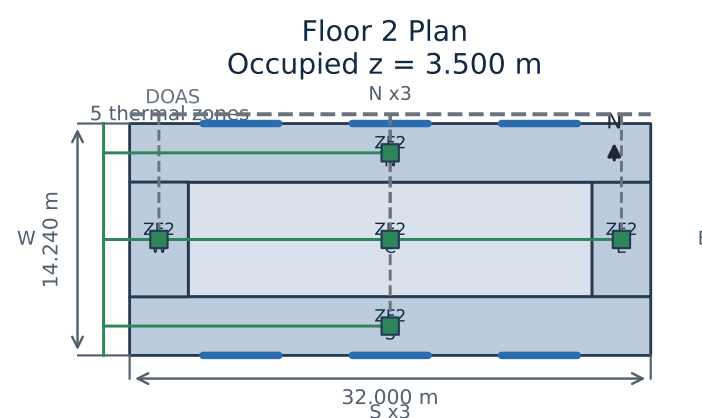






FCU + DOAS Service Overlay

System topology overlaid on plan, roof, facade, and section views

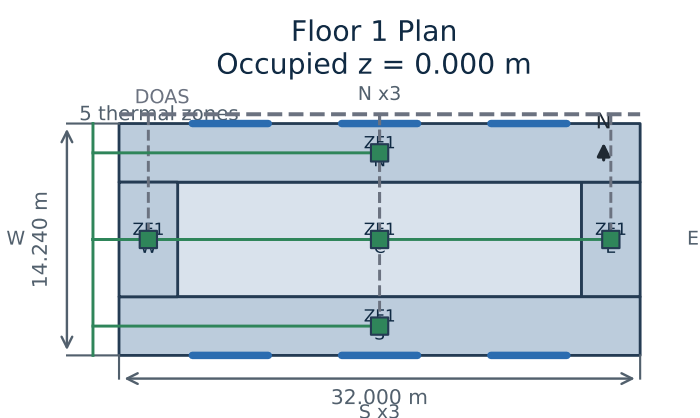


FCU + DOAS Service Overlay

Occupied stories served: 2
Per-floor terminals: 5
Model total terminals: 10
Roof equipment: DOAS AHU
Outdoor air distribution: one main spine plus zone branches
Vertical service: CHW/HW riser
Section emphasis: separated DOAS duct shaft and CHW/HW pipe shaft
Building footprint: 32.000 m x 14.240 m
Roof elevation: 7.0000 m

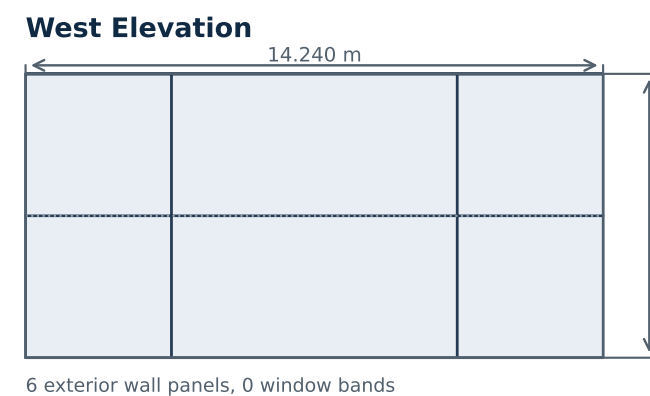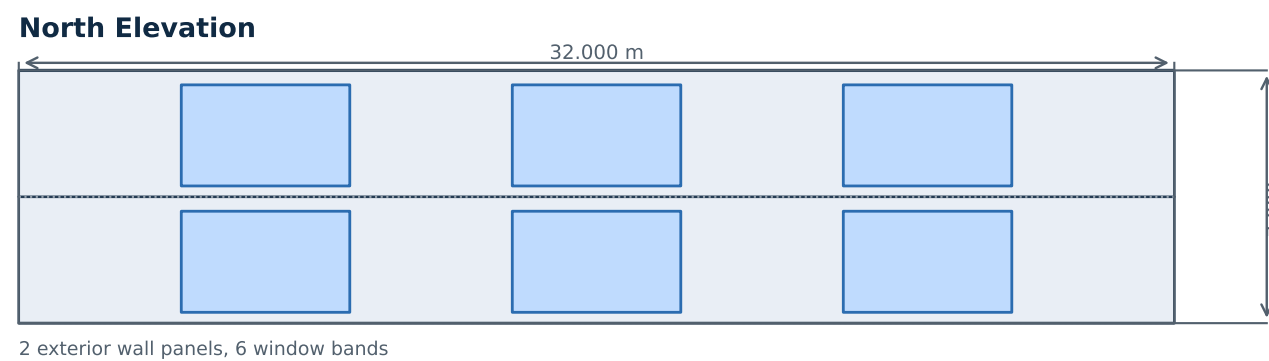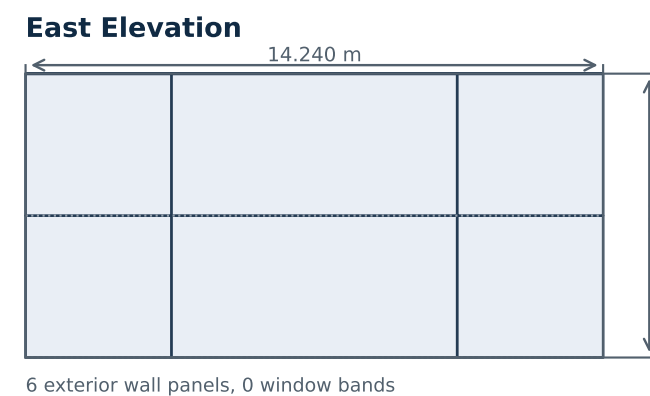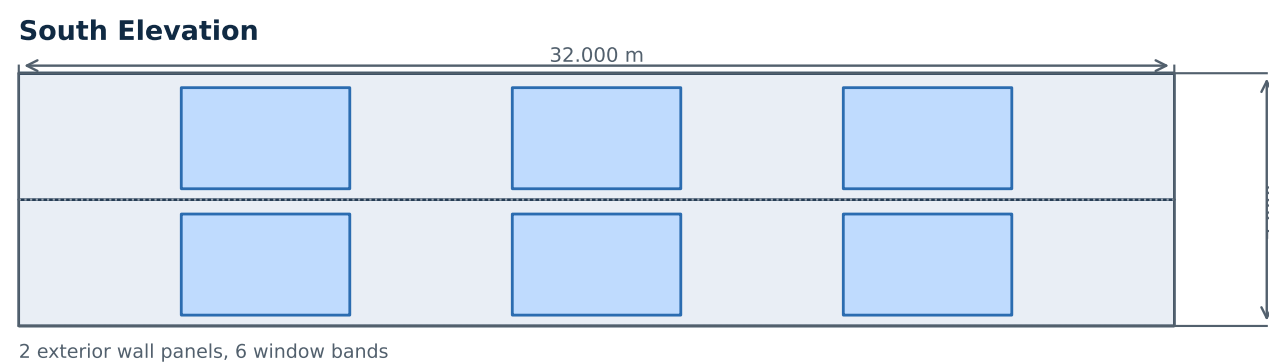

One fan-coil terminal per conditioned zone
Dedicated outdoor air spine and branch drops
Compact CHW/HW riser indicates plant-side service to floor terminals

Sectional Story Stack

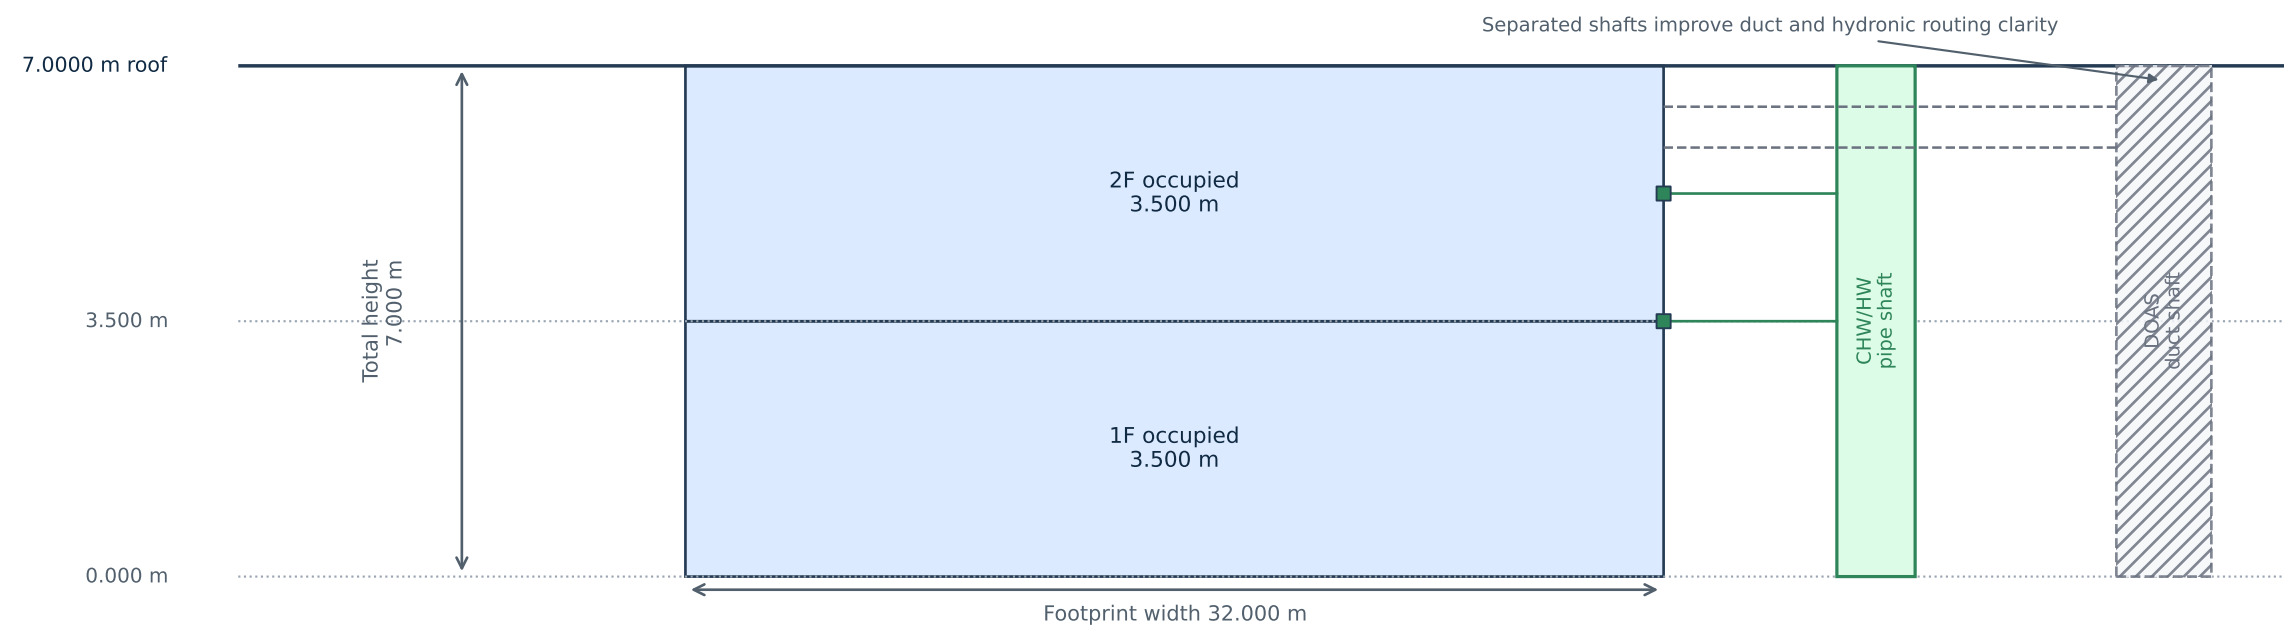

- Conditioned zone
- DOAS duct / shaft
- CHW/HW riser
- One fan-coil terminal per conditioned zone