
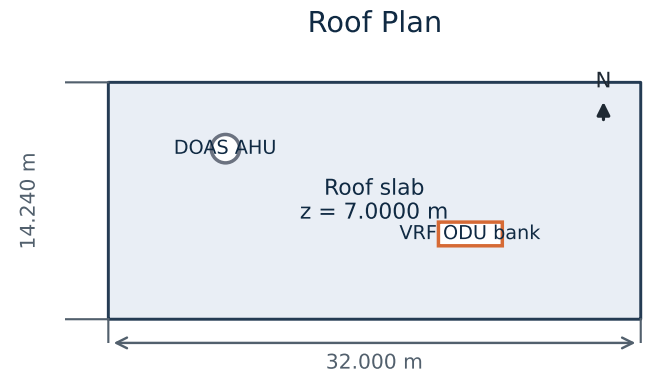
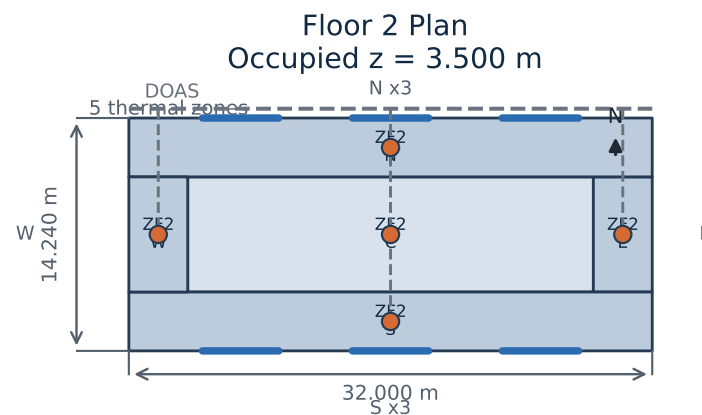






VRF + DOAS Service Overlay

System topology overlaid on plan, roof, facade, and section views

VRF + DOAS Service Overlay

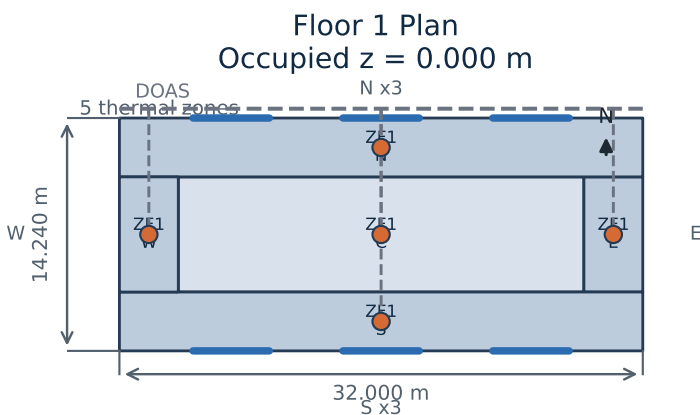


Occupied stories served: 2
Per-floor terminals: 5
Model total terminals: 10
Roof equipment: DOAS AHU, VRF ODU bank
Outdoor air distribution: one main spine plus zone branches
Vertical service: Refrigerant riser
Facade emphasis: concentrated rooftop ODU bank on south elevation
Building footprint: 32.000 m x 14.240 m
Roof elevation: 7.0000 m

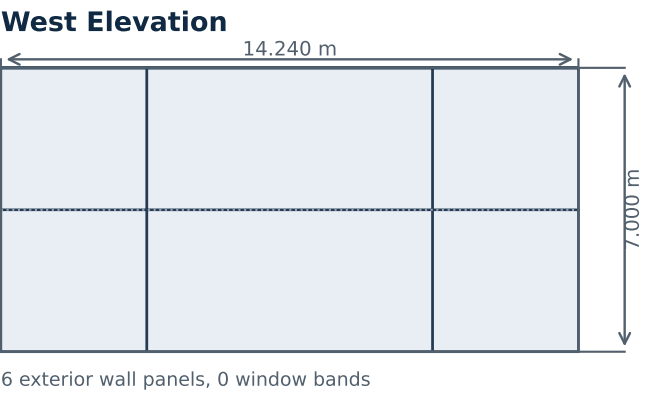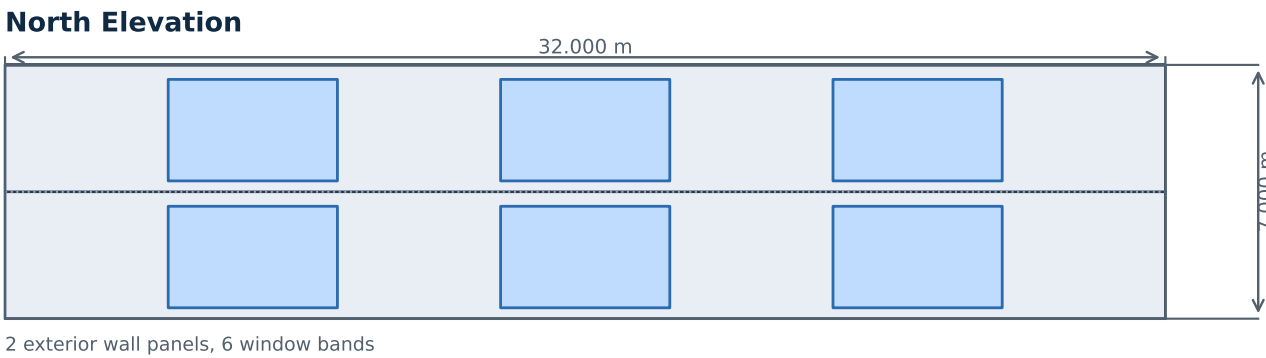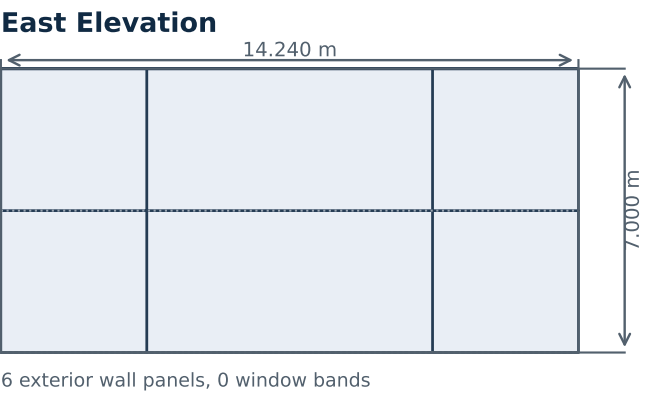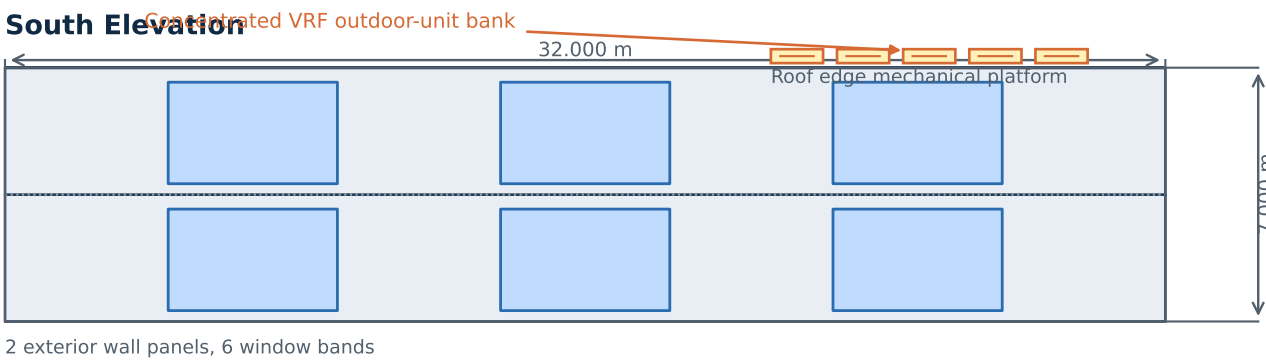

One VRF terminal per conditioned zone
Dedicated outdoor air spine and branch drops
Shared VRF outdoor unit serves all terminals on the model branch

Sectional Story Stack

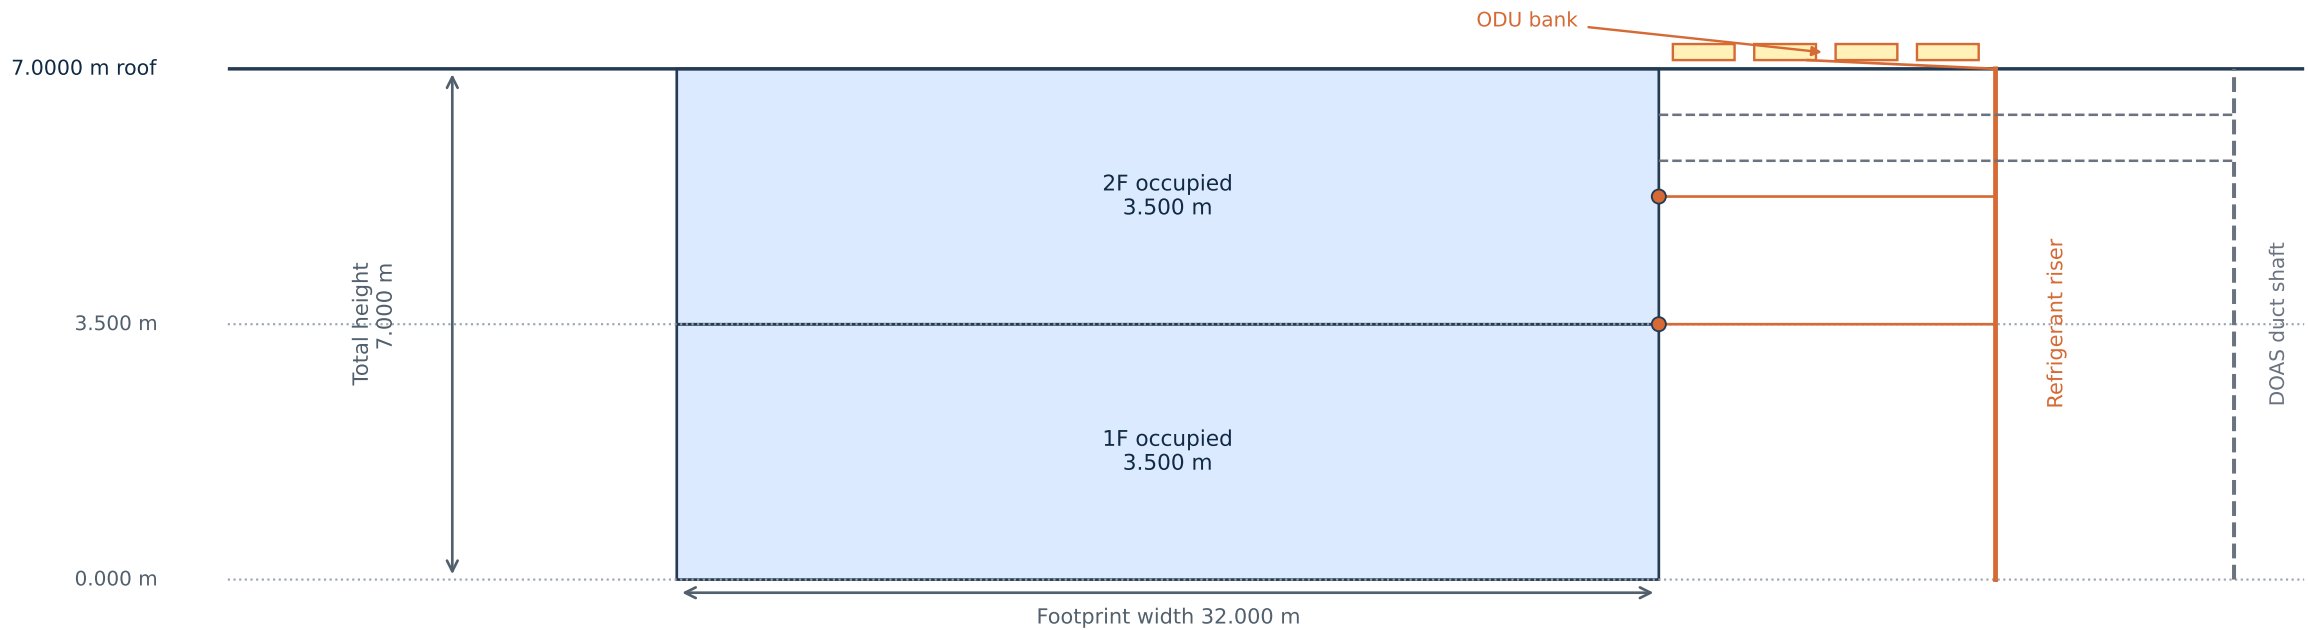

- Conditioned zone
- DOAS duct / shaft
- Refrigerant riser
- One VRF terminal per conditioned zone